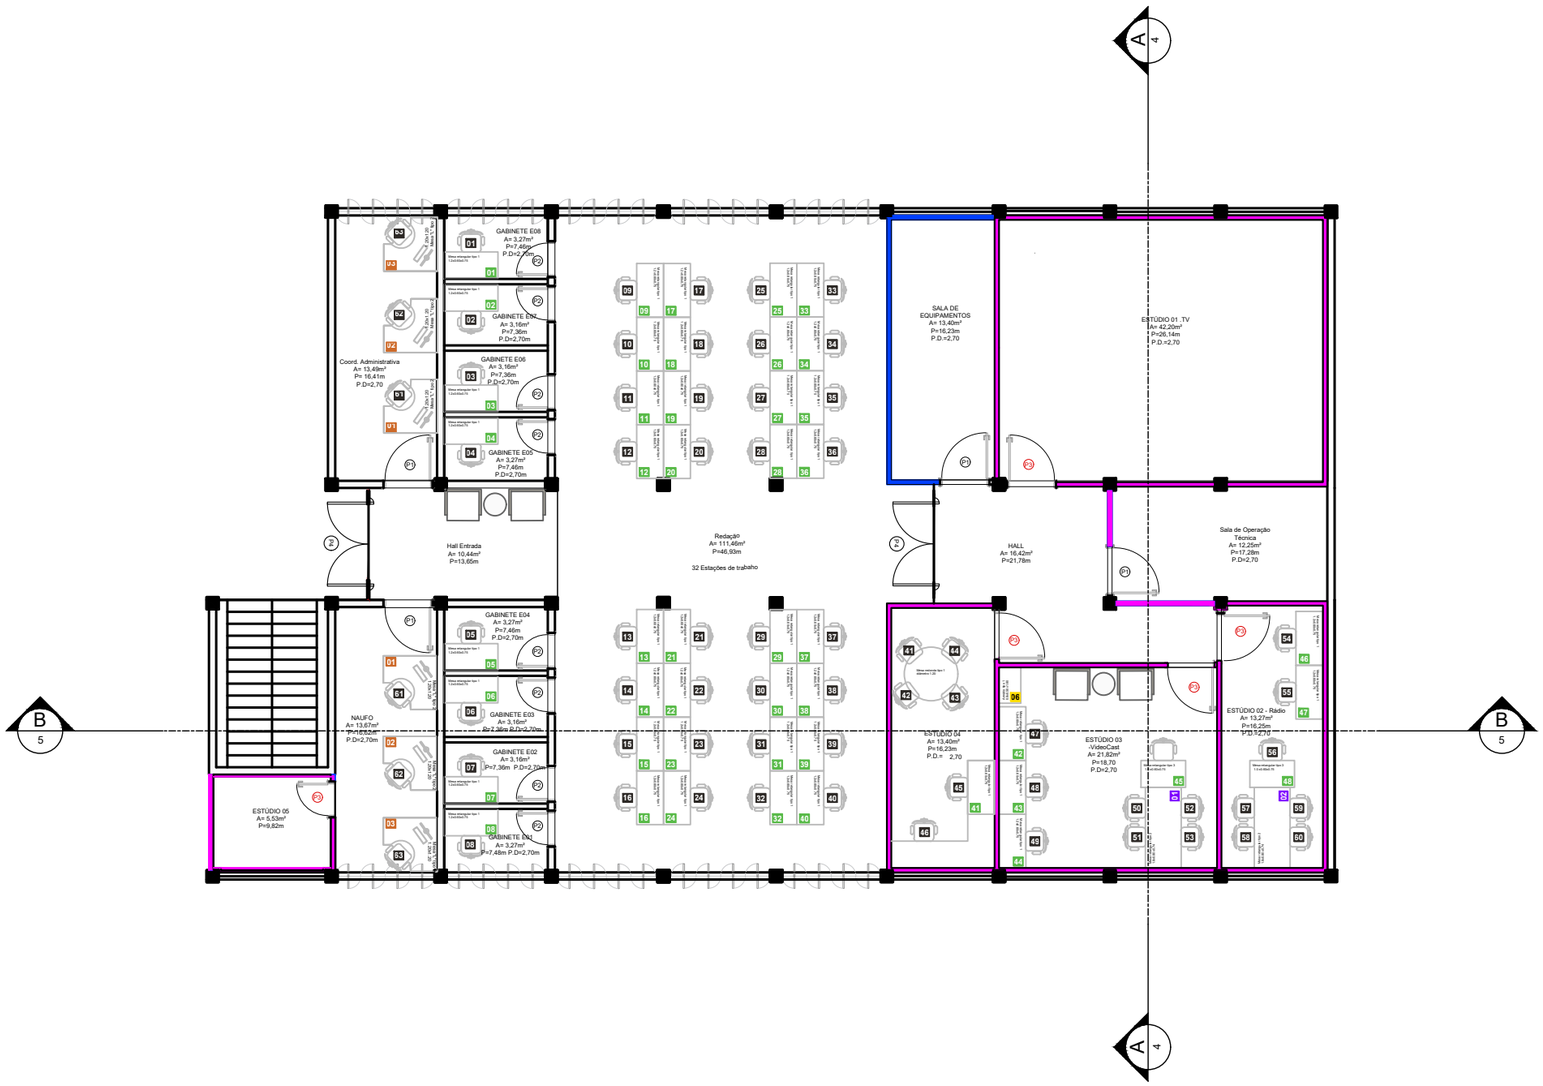


LEGENDA DE MOBILIÁRIO	
Mesa retangular tipo 1 1.2x0.60x0.75	48 un
Mesa "L" tipo 2 1.20x1.20	3 un
Cadeira modelo único	63 un
Armário tipo 1 0.8x0.50x1.60	6 un
Armário tipo 3 0.8x0.50x2.10	1 un
Mesa retangular tipo 2 1.8x0.80x0.74	2 un

LEGENDA DE PAREDE


- parede de drywall de 10cm - ISOLAMENTO ACÚSTICO
- parede de drywall de 10cm.
- parede existente.
- (P3) portas de 1x2,10 isolamento acústico.

① Planta Layout
1:100

Universidade Estadual de Goiás

Planta Layout
Crialab - arquivo UEG
escala: 1/100
revisão: 00

01

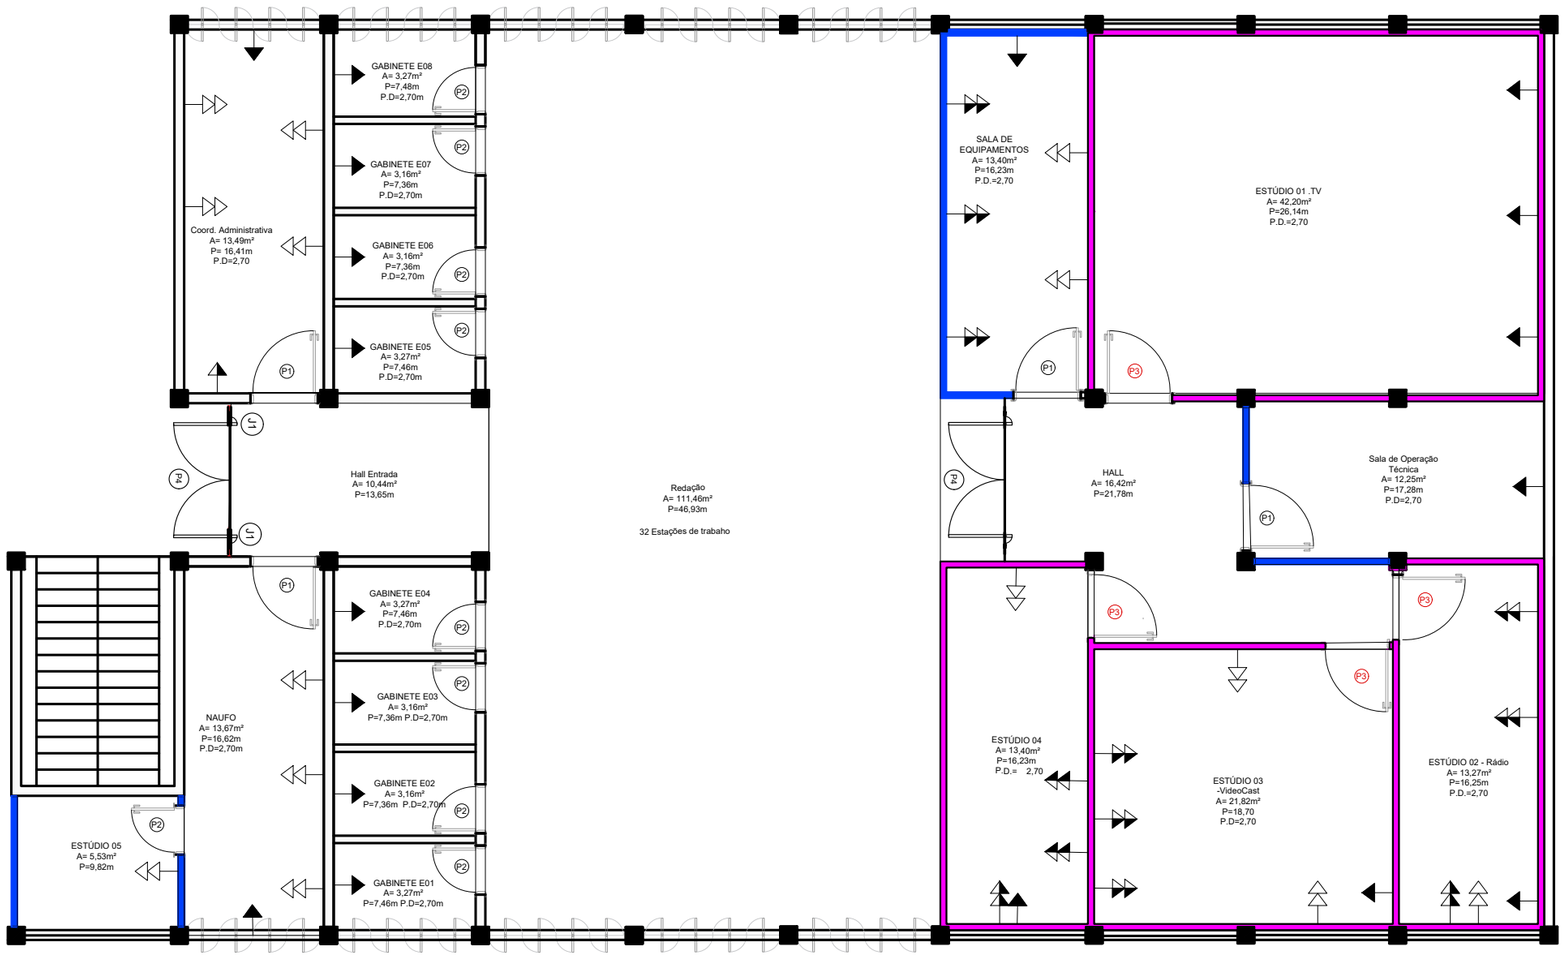

QUADRO AR CONDICIONADO				
Ambientes	Area (m²)	Pé direito	Volume	BTUs
Sala de reunião	13,5	2,85	38,475	12.000
Sala de coordena	13,5	2,85	38,475	12.000
Gabinete 01	3,28	2,7	8,856	7.000
Gabinete 02	3,16	2,7	8,532	7.000
Gabinete 03	3,16	2,7	8,532	7.000
Gabinete 04	3,28	2,7	8,856	7.000
Gabinete 05	3,28	2,7	8,856	7.000
Gabinete 06	3,16	2,7	8,532	7.000
Gabinete 07	3,16	2,7	8,532	7.000
Gabinete 08	3,28	2,7	8,856	7.000
Redação	111,46	2,85	317,661	2x 56.000
Estudio 01	41,33	2,7	111,591	32.000
Estudio 02	13,27	2,7	35,829	12.000
Estudio 03	21,82	2,7	58,914	16.000
Estudio 04	13,4	2,7	36,18	12.000
Sala de operaçã	12,25	2,7	33,075	12.000

Área (m²)	Ambiente Residencial	Ambiente Comercial
9 m²	7.000 BTUs	7.000 BTUs
12 m²	7.000 BTUs	9.000 BTUs
15 m²	9.000 BTUs	12.000 BTUs
20 m²	12.000 BTUs	16.000 BTUs
25 m²	15.000 BTUs	20.000 BTUs
30 m²	18.000 BTUs	24.000 BTUs
35 m²	21.000 BTUs	28.000 BTUs
40 m²	24.000 BTUs	32.000 BTUs
45 m²	27.000 BTUs	36.000 BTUs
50 m²	30.000 BTUs	40.000 BTUs
60 m²	36.000 BTUs	48.000 BTUs
70 m²	42.000 BTUs	56.000 BTUs

LEGENDA


- Energia - Baixa 30cm do piso
- Energia - Média 90cm do piso
- Energia - Alta ar concionado

② Planta Tomadas
1:100

Universidade Estadual de Goiás

Planta Tomadas
Crialab - arquivo UEG
escala: 1/100
revisão: 00

02

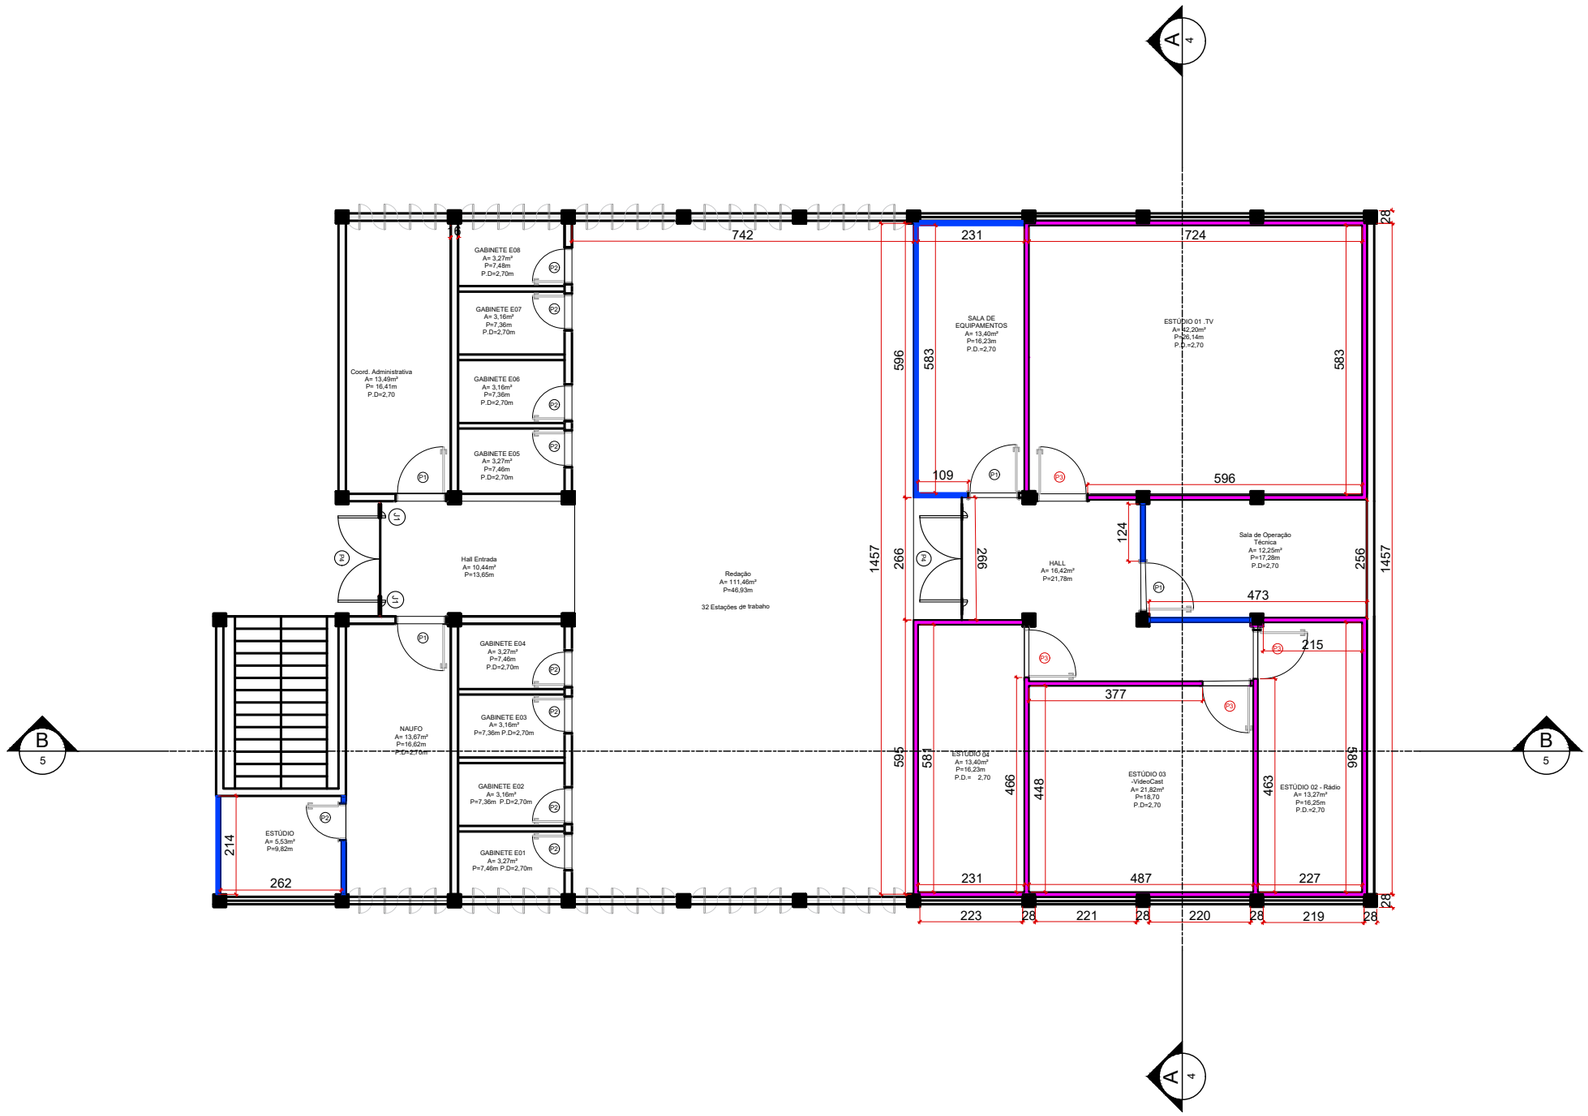

QUADRO DE ABERTURAS

Portas


Código	Quantidade	Comprimento	Altura
P1	4	1,0000	2,1000
P2	9	0,7000	2,1000
P3	4	1,0000	2,1000
P4	2	1,7900	2,1000

③ Planta Técnica
1:100


Universidade Estadual de Goiás

Planta Técnica
Crialab - arquivo UEG
escala: 1/100
revisão: 00

03

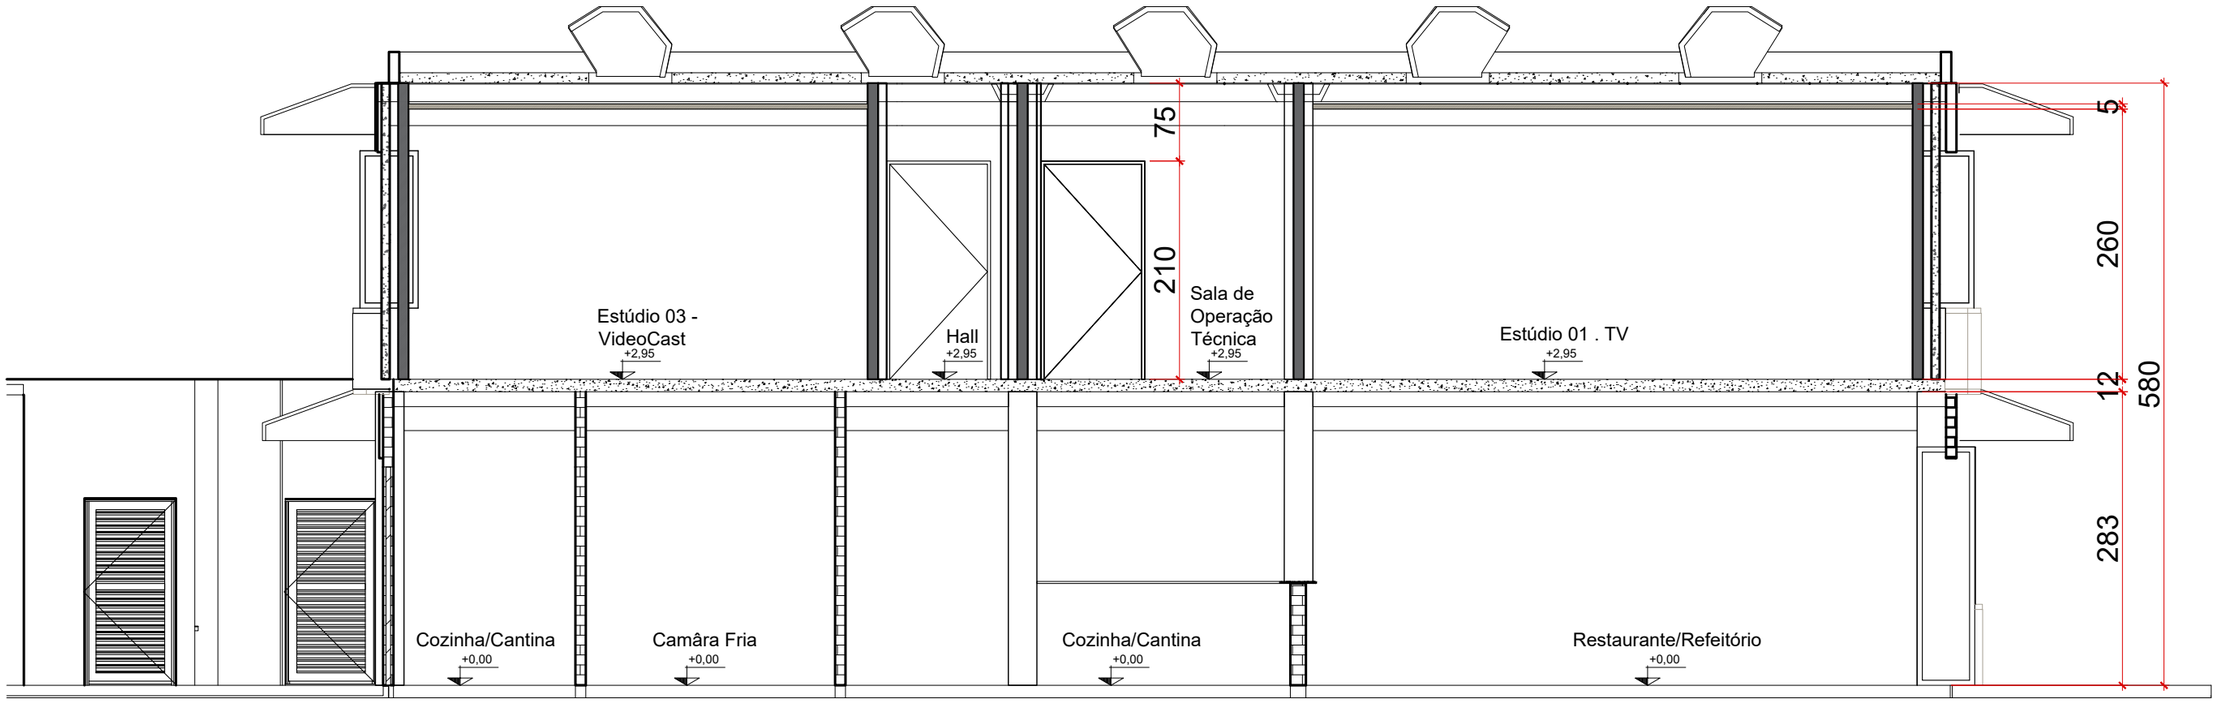

④ Corte A - A
1:100

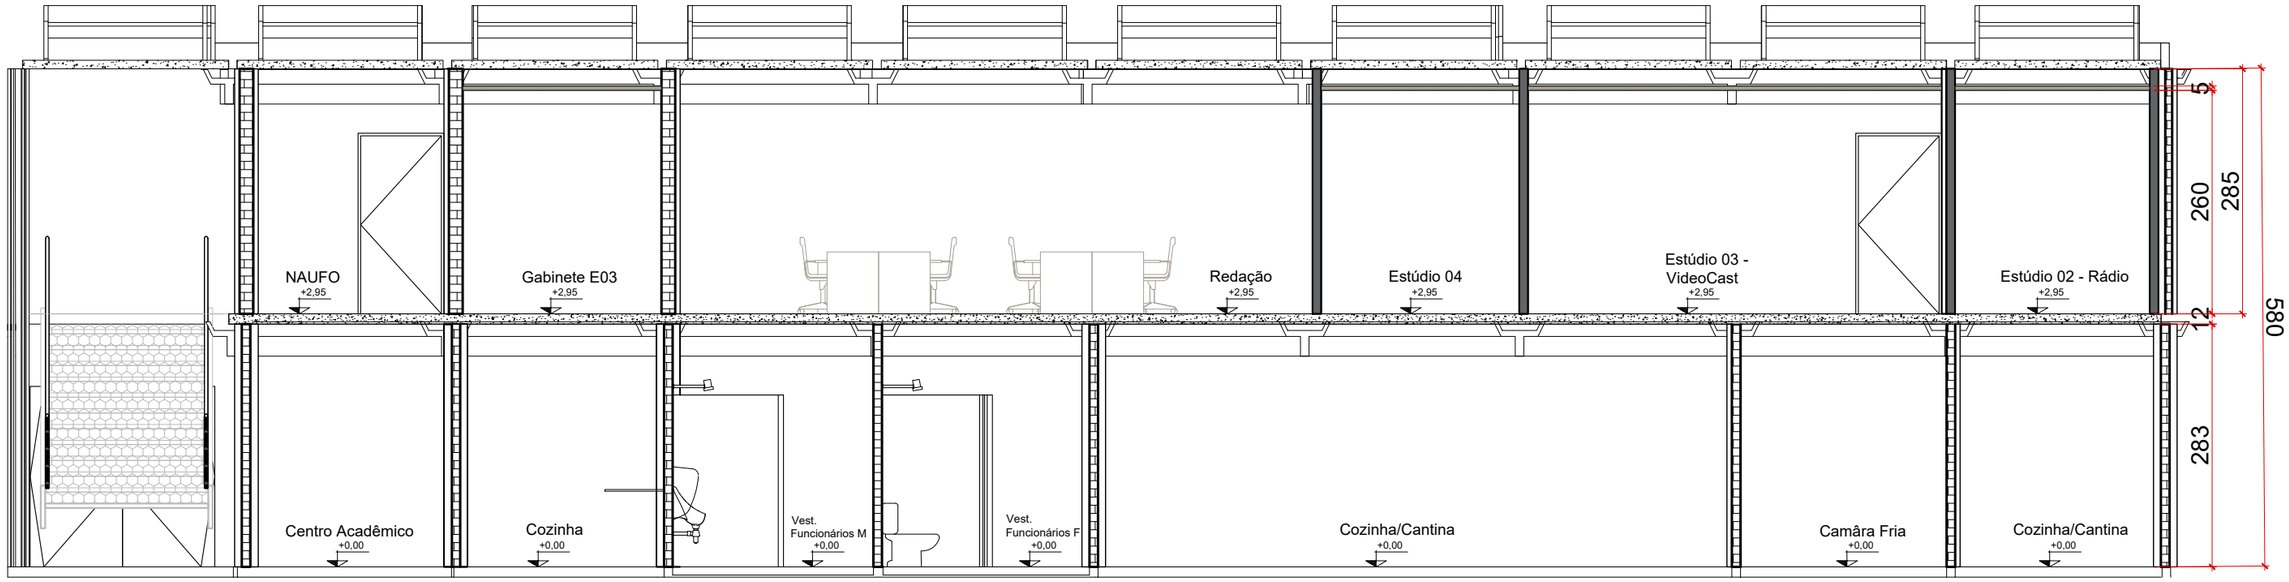

⑤ Corte B - B
1:100

Universidade Estadual de Goiás

Corte B-B
Crialab - arquivo UEG
escala: 1/100
revisão: 00

05